
RITNINGSFÖRTECKNING A-RITNING


Ritn. Nr.	Ritningstyp	Rit. datum	Rev.	Rev. datum	Anmärkningar
11-100152-A10	PLANER, SEKTION	2024-05-06			
11-100152-A11	FASADER	2024-05-06			
11-100152-A12	FASADER	2024-05-06			
11-100152-A13	FASADER 1:200	2024-05-13			
11-100152-A14	SITUATIONSPLAN	2024-05-06	A	2024-06-26	CARPORT/VÄXTHUS BORT
11-100152-A15	DETALJERAD SEKTION	2024-05-06			

Götenehus


BOX 17, 533 21 GÖTENE, TEL. 0511-34 56 00
WWW.GOTENEHUS.SE

Signatur	Projektnummer	Hustyp
ASL	11-100152	DJURÅS LADA OFFERT

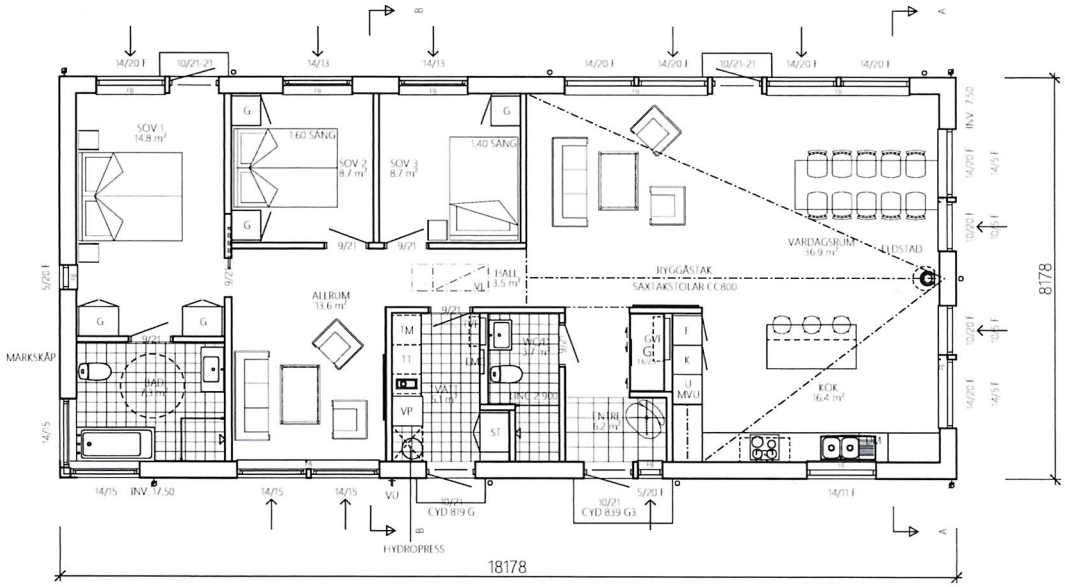

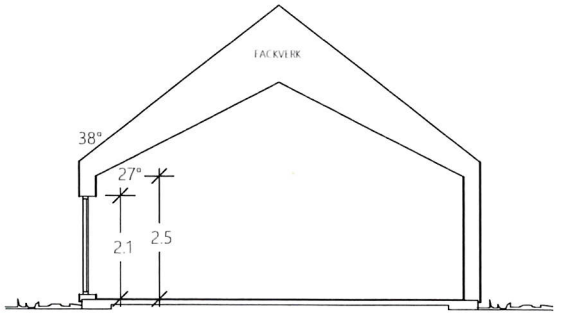

SEKTION A-A

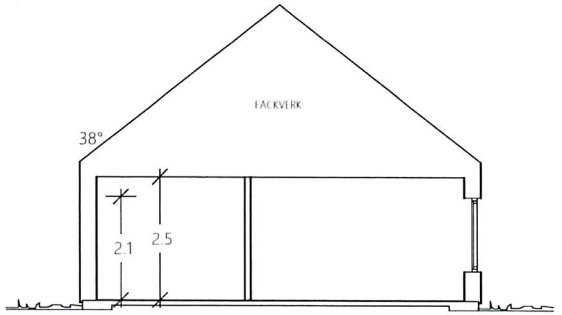

SEKTION B-B

ENTREPLAN

BYA = 148.7 m²
BRA I = 131.3 m²
BTA = 148.7 m²

TVF=SKÅP FÖR TAPPVATTEN FÖRDELARE OCH VATTENMÄTARE
GVF=SKÅP FÖR GOLVVÄRME FÖRDELARE
FM=FASADMÄTARSKÅP
EMC alt EC o MC=EL- OCH MEDIACENTRAL
VU=VATTENUPPKASTARE
VL=VINDSLUCKA
VF=SKÅP FÖR VATTEN FÖRDELARE
HT=HANDDUKSTORK
HTV=VATTENBUREN HANDDUKSTORK
TF=TAKFÖNSTER
F=FAST FÖNSTER
FB=FÖNSTERBÄNK
IL=INSP.LUCKA
=STUPRÖR
=RÖRUTLOPP ELUTTAG
=RÖRUTLOPP YTTERBELYSNING VÄGG
=RÖRUTLOPP YTTERBELYSNING TAK
=RADIATOR
=INST.UTRYMME/SCHAKT/INST.LÅDA
=SYNLIG BALK
=BÄRANDE INNERVÄGG
=BÄRANDE INNERVÄGG ISOLERAD
=INNERVÄGG
=INNERVÄGG ISOLERAD
=KLINKER
=TILLUFTSVENTIL FÖNSTERKARM/VÄGG
UTVÄNDIGA TRAPPOR INGÅR EJ

RÖKRÖR AV TYPGODKÄNT FABRIKAT.
EV. TILLUFT TILL ELDSTAD,
SE TILLVERKARENS ANVISNINGAR


1:100 10m

REG	ANT	REGISTRERINGEN AVSER	SIGN.	DATUM


Götenehus
BOX 17, 533 21 GÖTENE, TEL. 0511-34 56 00

BYGGLOVSHANDLING

RITAD AV/GRANSKAD AV	ARBETSNUMMER	SKALA 1:100	
ASL	11-100152		
GÖTENE	HUSTYP	RITNINGSNUMMER	REG
2024-05-06	DJURÅS LADA OFFERT	11-100152-A10	

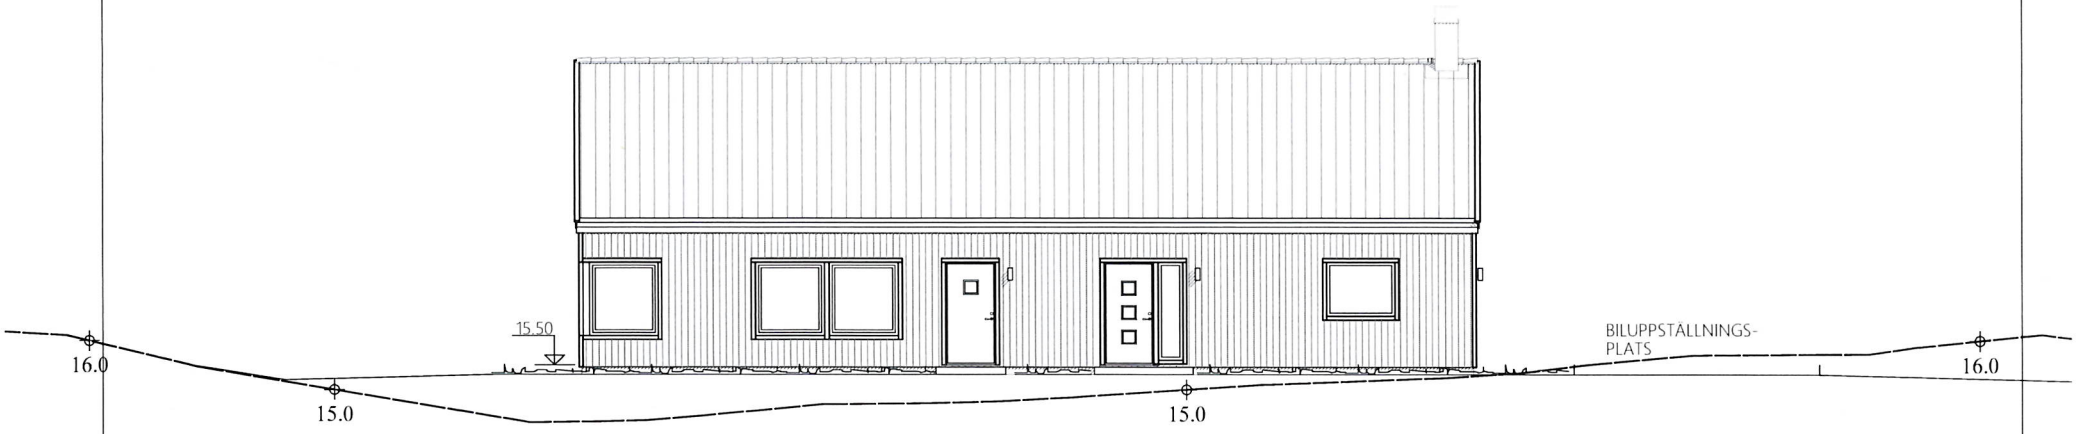

FASAD MOT NORDOST

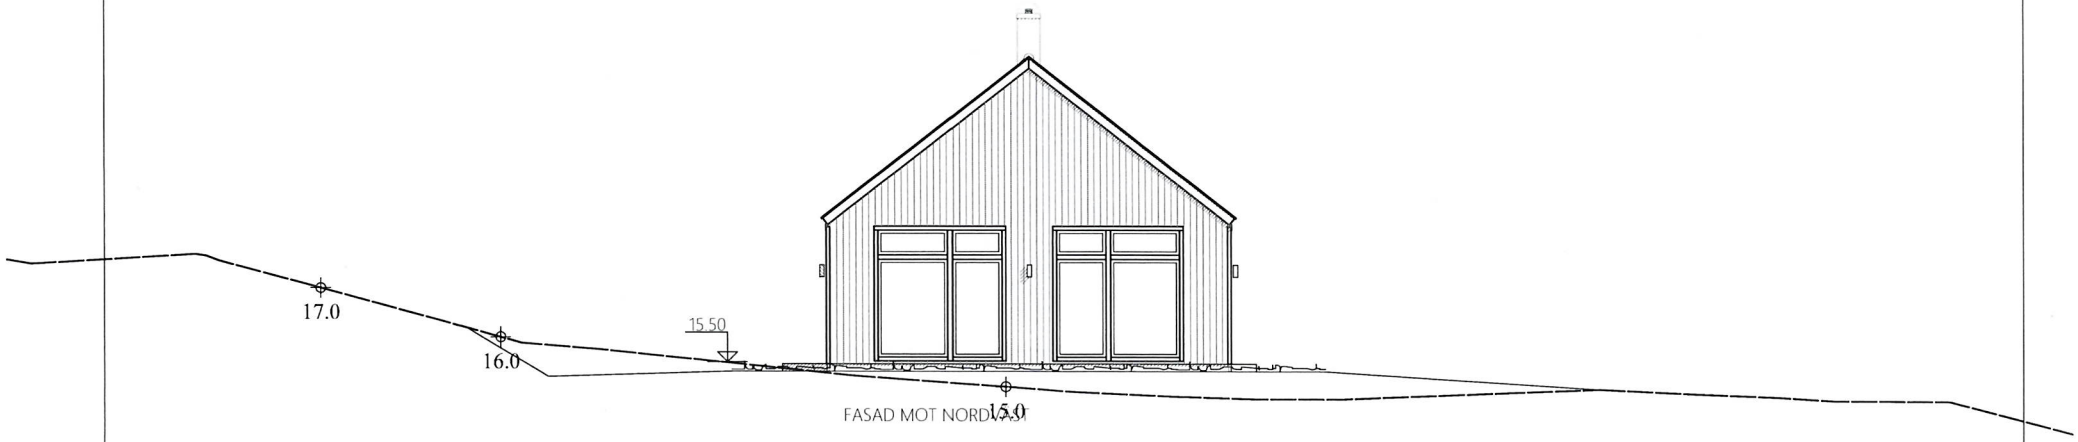

FASAD MOT NORDVÄST

BEFINTLIG MARK
BLIVANDE MARK


1:100 10m

REG	ANT	REGISTRERINGEN AVSER	SIGN	DATUM


Götenehus
BOX 17, 533 21 GÖTENE, TEL. 0511-34 56 00

BYGGLOVSHANDLING

RITAD AV/GRANSKAD AV	ARBETSNUMMER		
ASL	11-100152		SKALA 1:100
GÖTENE	HUSTYP	RITNINGSNUMMER	REG
2024-05-06	DJURÅS LADA OFFERT	11-100152-A11	

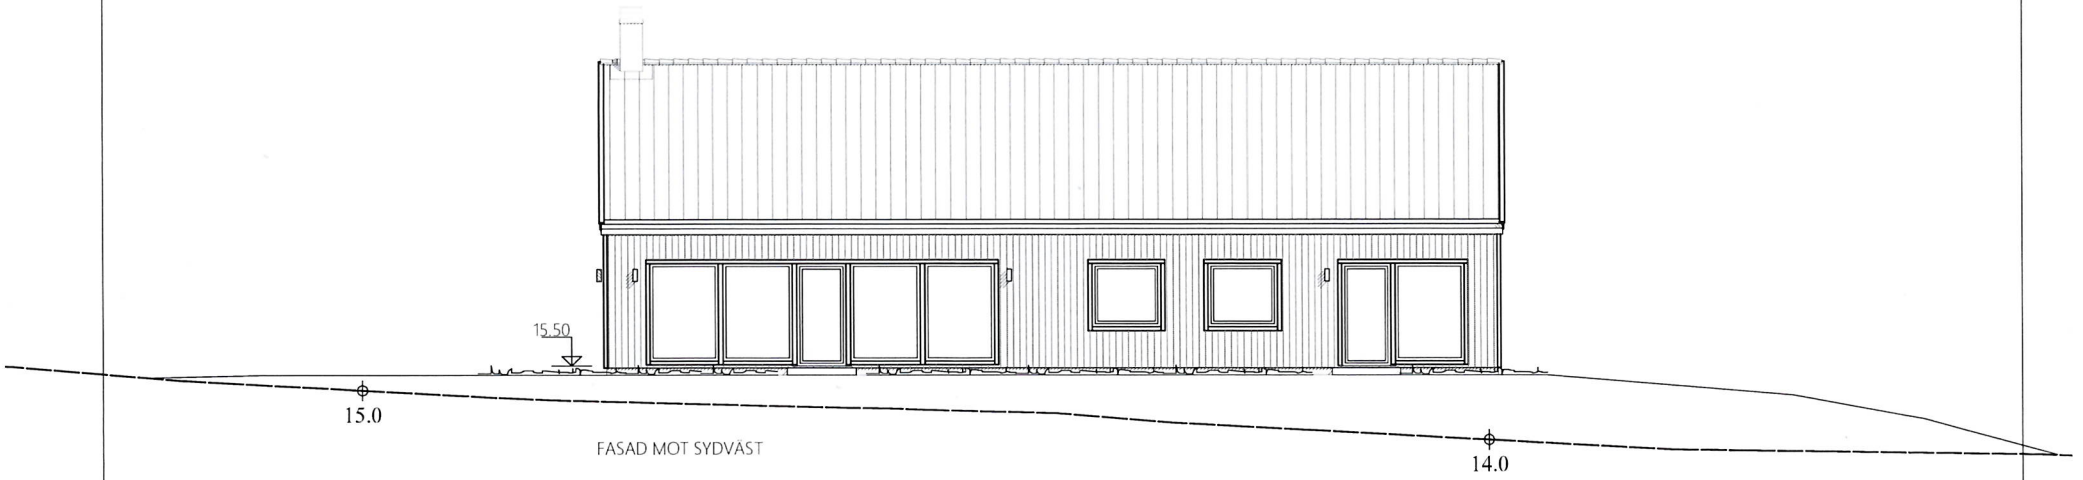

FASAD MOT SYDVÄST

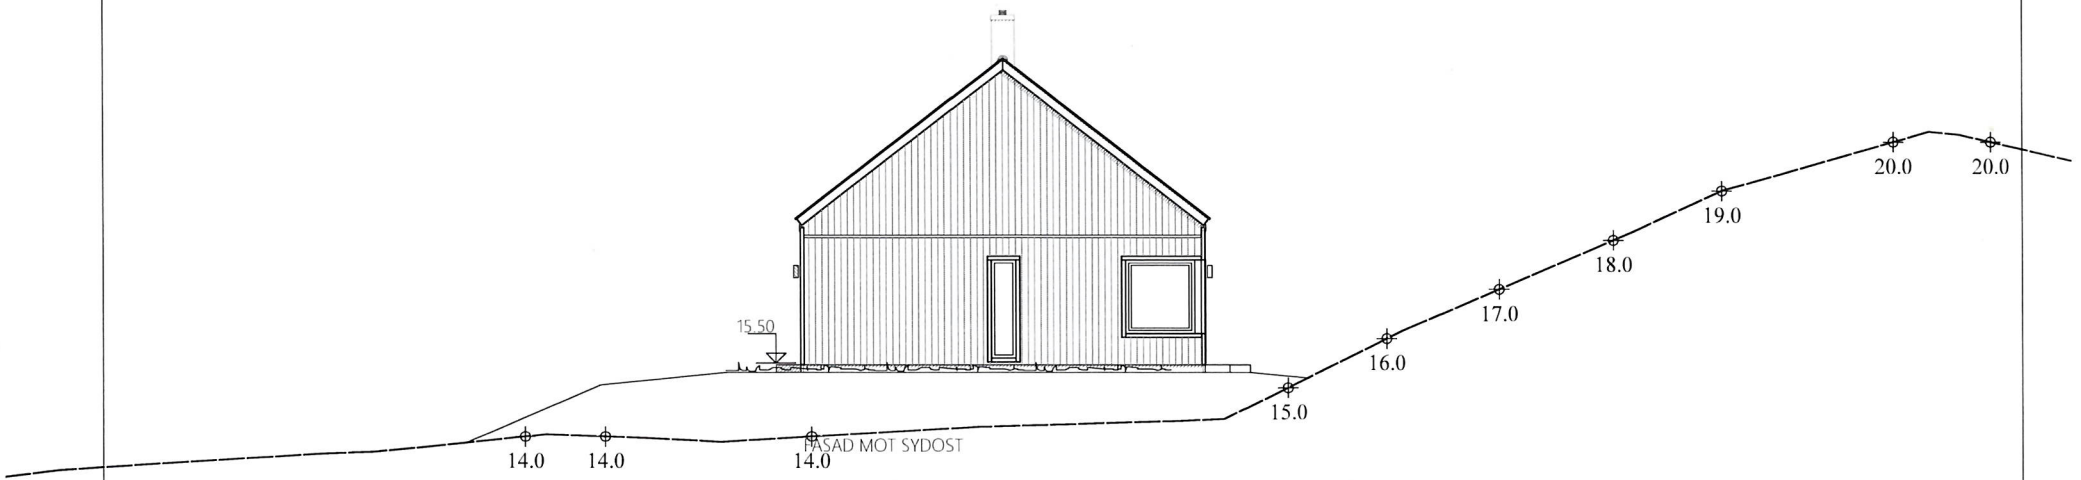

FASAD MOT SYDOST

BEFINTLIG MARK
BLIVANDE MARK


1:100 10m

REG	ANT	REGISTRERINGEN AVSER	SIGN.	DATUM

Götenehus
BOX 17, 533 21 GÖTENE, TEL. 0511-34 56 00

BYGGLOVSHANDLING

RITAD AV/GRANSKAD AV	ARBETSNUMMER	SKALA 1:100	
ASL	11-100152		
GÖTENE	HUSTYP	RITNINGSNUMMER	REG
2024-05-06	DJURÅS LADA OFFERT	11-100152-A12	

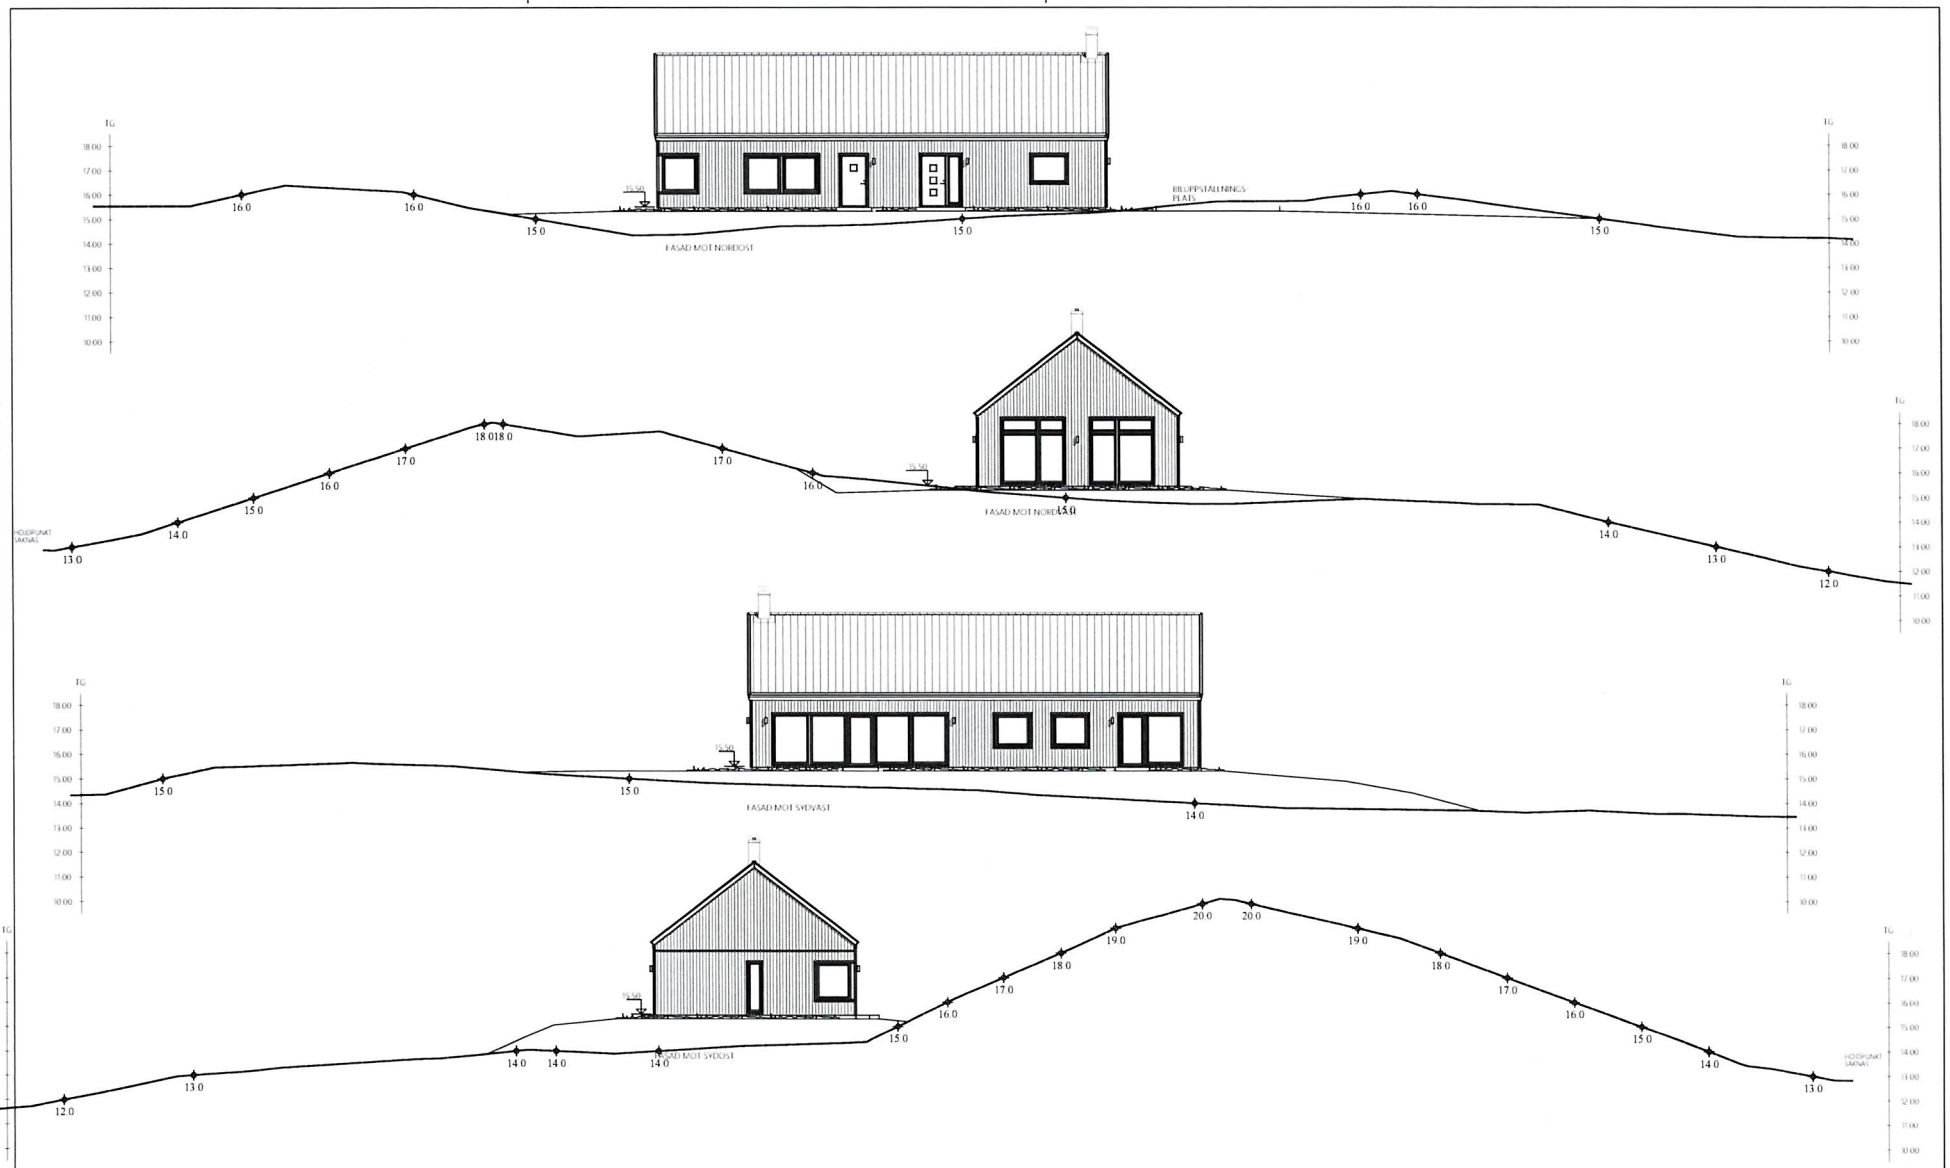

REG	ANT	REGISTRERINGEN AVSER	SIGN	DATUM

Götenehus
BOX 17, 533 21 GÖTENE, TEL 0511-34 56 00

BYGGHANDLING

RITAD AV/GRANSKAD AV	ARBETSNUMMER	SKALA 1:200
ASL	11-100152	
GÖTENE	HUSTYP	RITNINGSNUMMER / REG
2024-05-13	DJURÅS LADA OFFERT	11-100152-A13

Nybyggnadskarta - typ B

HÄVERÖ-BERGBY 1:28 och 1:29

NORRTÄLJE KOMMUN

Upprättad den 10 januari 2024
Kartans giltighetstid är två år

Niklas Berggren
Mätningsingenjör
Granskad av:Wassim Gorgis


Koordinatsystem
i plan: SWEREF 99 18 00
i höjd: RH 2000

Anvisning på plats av el- och telekablars läge är nödvändig innan grävning får påbörjas.
Beställ på www.ledningskollen.se


Dnr: BoM 2024-000006
Areal: 2 620 m² resp. 2 526 m²
Adress: Trästa broväg 126 resp. 124
Skala: 1:500 / A3

Teckenförklaring

TÄLJE	Traktnamn		Ägoslagsgräns
3:9	Fastighetsbeteckning		Berg kantlinje
— — —	Fastighetsgräns		Blandskog
— — —	Traktgräns		Lövskog
	Uthus	//	Åker
= = = =	Väg		Berg i dagen
	Nivåkurvor		Rättigheter
20,5	Höjdpunkt		

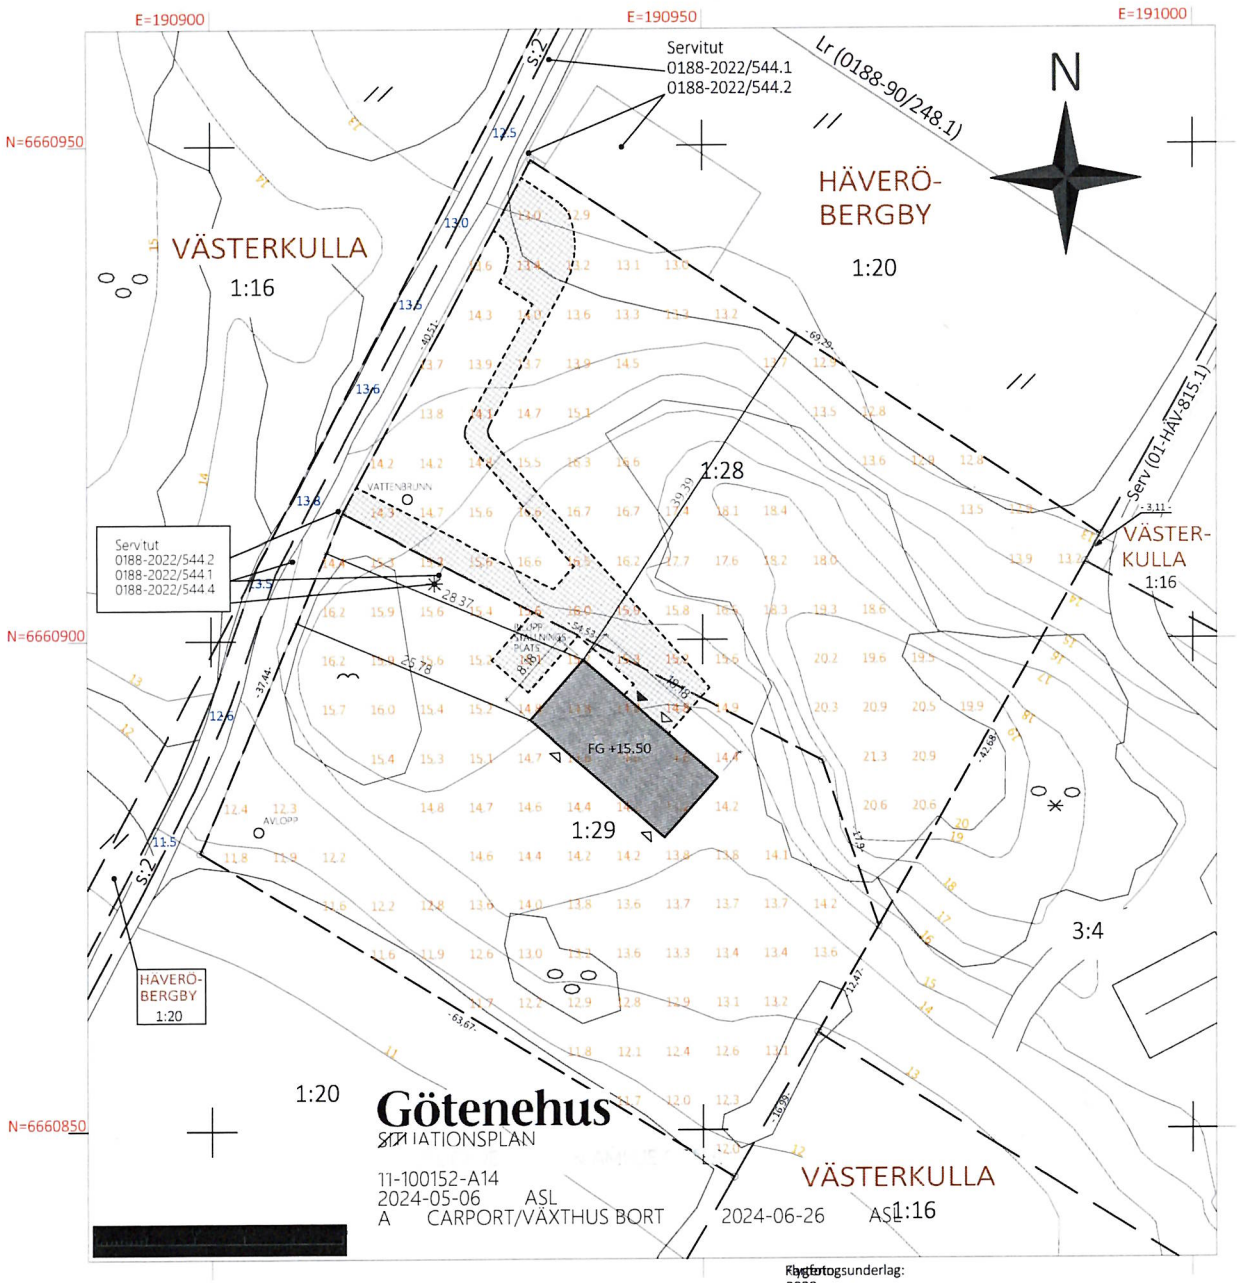


Flygfotosunderlag: Lm's flygfoto 2020, samt kontroll mot Lm's flygfoto 2023

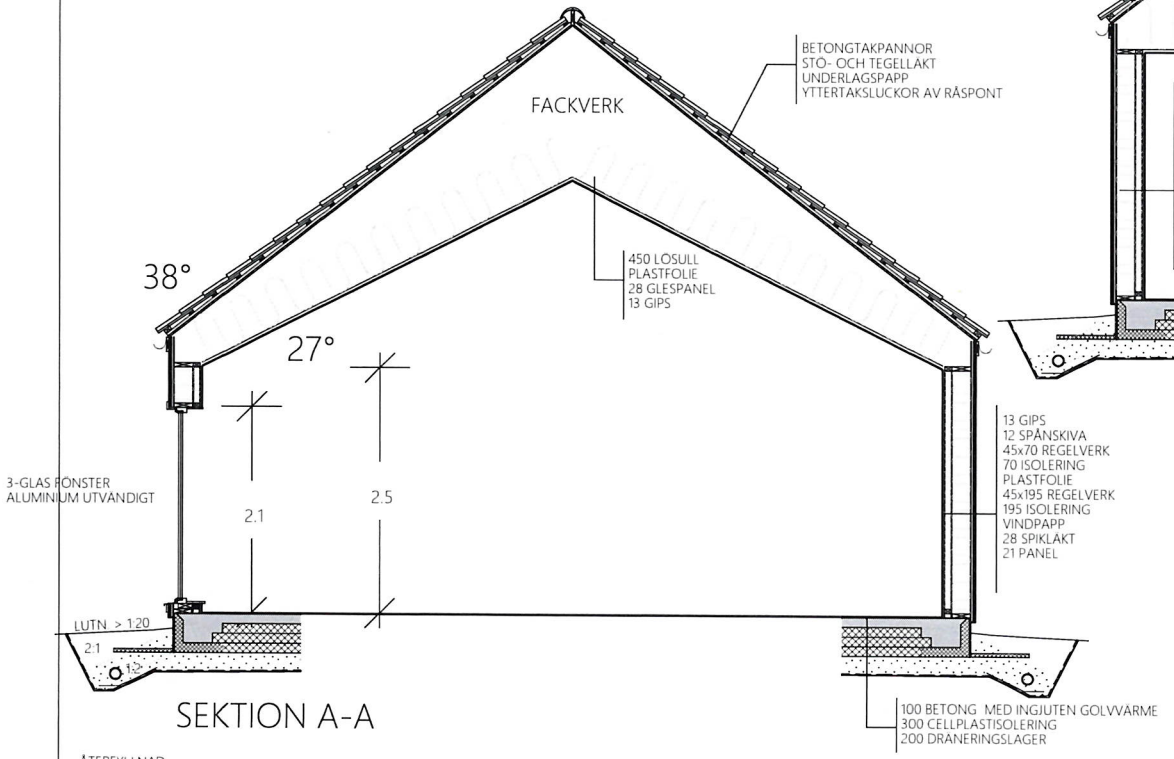

SEKTION A-A

ÅTERFYLLNAD
(VID ÅTERFYLLNAD MED JORD
SKALL DRÄNERINGSLAGRET
SKYDDAS MED FIBERDUK)

DRÄNERINGSRÖR TYP DSA ø 100/117 EL. LIKVÄRDIGT
LÄGGES MED LUTNING > 1:200 ENL. VA-SIT.PLAN.
I LEDNINGENS LÄGSTA PUNKT LÄGGES
EN SLAMSAMLINGSBRUNN OCH I HÖGSTA PUNKTEN
ANORDNAS SPOLBRUNNAR FÖR RENSNING &
FUNKTIONSKONTROLL
VID UNDERGRUND AV SAND/LERA ELLER SILT BÖR GEOTEXTIL ANVÄNDAS

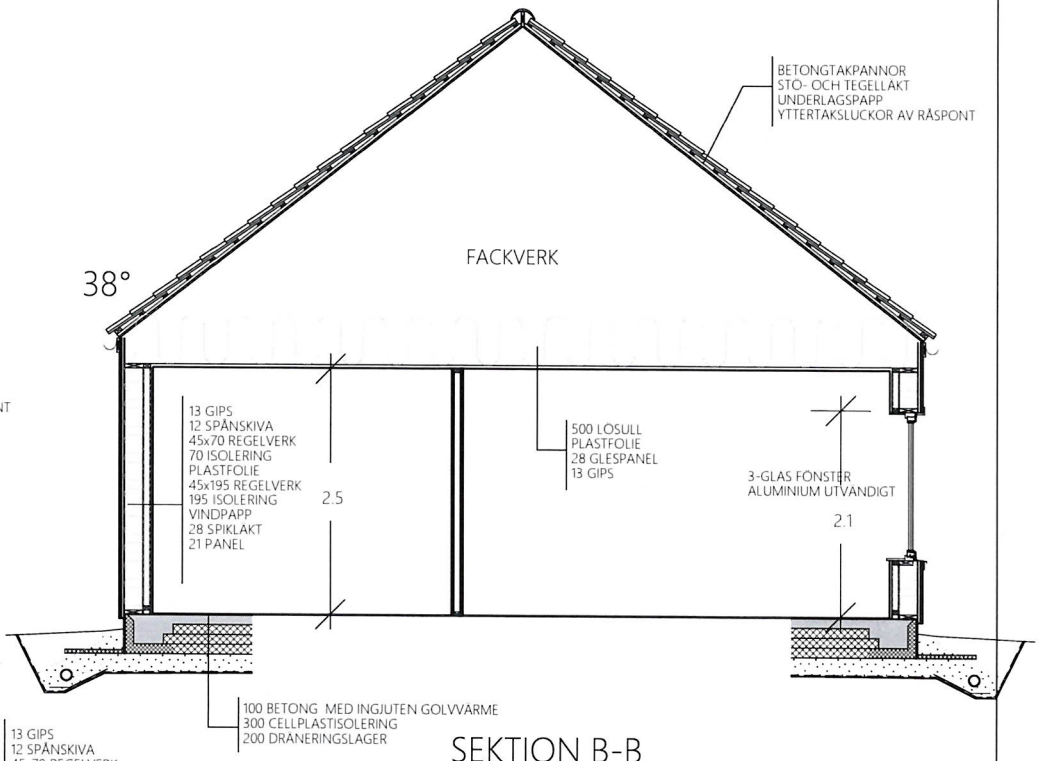

SEKTION B-B

ÅTERFYLLNAD
(VID ÅTERFYLLNAD MED JORD
SKALL DRÄNERINGSLAGRET
SKYDDAS MED FIBERDUK)

DRÄNERINGSRÖR TYP DSA ø 100/117 EL. LIKVÄRDIGT
LÄGGES MED LUTNING > 1:200 ENL. VA-SIT.PLAN.
I LEDNINGENS LÄGSTA PUNKT LÄGGES
EN SLAMSAMLINGSBRUNN OCH I HÖGSTA PUNKTEN
ANORDNAS SPOLBRUNNAR FÖR RENSNING &
FUNKTIONSKONTROLL
VID UNDERGRUND AV SAND/LERA ELLER SILT BÖR GEOTEXTIL ANVÄNDAS

REG	ANT	REGISTRERINGEN AVSER	SIGN.	DATUM

Götenehus
BOX 17, 533 21 GÖTENE, TEL. 0511-34 56 00

BYGGLOVSHANDLING

RITAD AV/GRANSKAD AV	ARBETSNUMMER	SKALA 1:50
ASL	11-100152	
GÖTENE 2024-05-06	HUSTYP DJURÅS LADA OFFERT	RITNINGSNUMMER 11-100152-A15 REG