Projekt : 20 ENKELSTUGAN, 2011

Konstruktionsvirke ----------

Syll

Typ	B x H	Längd	Vinkel	Nr	Antal
201	45x 120	7247	90 90	10	2
201	45x 120	5086	90 90	10	2

Hammarband

Typ	B x H	Längd	Vinkel	Nr	Antal
211	45x 120	7247	90 90	20	2
211	45x 120	5086	90 90	20	2

Reglar

Typ	B x H	Längd	Vinkel	Nr	Antal
221	45x 120	2354	90 90	30	51

Dimension	Längd (m)	
45 x 120	28.3	
45 x 70	75.0	Mellanväggar

Ö/U-slag

Typ	B x H	Längd	Vinkel	Nr	Antal
231	45x 120	1155	90 90	40	6
231	45x 120	999	90 90	42,40	4
231	45x 120	900	90 90	41	1
231	45x 120	500	90 90	40	2

Balk

Typ	B x H	Längd	Vinkel	Nr	Antal
241	45x 220	990	90 90	50	1

Läkt

Dimension	Längd (m)
45 x 45	175.0
34 x 70	200.0

Panel

Typ	B x H	Längd	Vinkel	Nr	Antal
261	22x 170	3000	90 90	0	68
261	16x 56	3000	90 90	0	66

Dimension	Längd (m)	
22 x 170	255.0	panel bottenbrädor
15 x 95	785.0	inv väggpanel
16 x 45	245.0	panel lockläkt
22 x 120	55.0	foderbrädor
22 x 95	8.0	dropplist
16 x 70	120.0	sockelspjälor
16 x 45	20.0	sockelbrädor
22 x 95	15.0	sockelbrädor
15 x 95	400.0	inv takpanel
22 x 95	367.0	vindsgolv
22 x 145	24.0	smygbrädor
	27.0	sockellist
	44.0	taklist
	57.0	foderlist
	23.0	smyglist


Byggskivor ------------------------------
Byggn. skiva
Tjocklek Dimension Antal
13 1200x 2400 10
Dimension Längd (m)
4.5 x 50 162.5 K-board

Kantbjälke
Dimension Längd Vinkel Nr Antal
45 x 220 4996 90 90 100 2 K24/C24
45 x 220 3743 90 90 101 4 K24/C24

Modulbjälke
Dimension Längd Vinkel Nr Antal
45 x 220 3743 90 90 303 2 K24/C24
45 x 170 4996 90 90 300 11 K12/C14
45 x 170 675 90 90 305 18 K12/C14
45 x 70 7486 90 90 301 2 bjälklagsregel
45 x 70 4906 90 90 302 2 bjälklagsregel
45 x 70 630 90 90 306 4 bjälklagsregel
19 x 100 4906 90 90 304 11 blindbottenbrädor
19 x 100 603 90 90 307 13 blindbottenbrädor
28 x 95 300 90 90 15 NTR/A

Kortling
Dimension Längd Vinkel Nr Antal
19 x 100 555 90 90 0 586 blindbotten
45 x 120 4996 90 90 0 2 undre syll
Dimension Längd (m)
28 x 95 400.0 lm slätspont golv


Tak
Dimension Längd (m)
45 x 120 9.0 nockplanka
25 x 25 110.0 ströläkt
25 x 38 183.0 bärläkt
22 x 95 18.0 takfotsbrädor
Dimension Längd Vinkel Nr Antal
50 x 50 3900 90 90 0 4 trekantlist
45 x 45 3900 90 90 0 4 gavelläkt
22 x 170 3900 90 90 0 4 vindskivor NTR/AB
22 x 95 3900 90 90 0 4 vindskivor NTR/AB
22 x 95 3900 90 90 0 4 vattbrädor NTR/AB
23 x 95 8230 90 90 0 88 råspont yttertak
45 x 220 7247 90 90 0 2 K24/C24 avväxlingsbalk
45 x 95 675 90 90 0 12 K12/C14 stödben

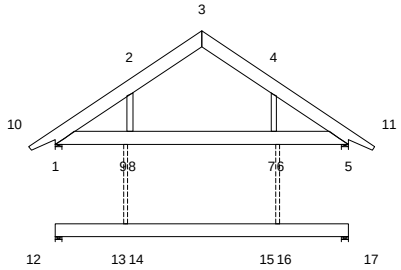


FRÅN-TILL	SPEC.	FIGUR

ÖVERRAM

10 - 3	Dimension:	45 x 220
11 - 3	Kvalitet:	C24
	Längd total:	3600 mm
	Längd centrum:	3527 mm
	Antal per konstruktion:	2 st
	Antal totalt:	14 st (7v,7h)

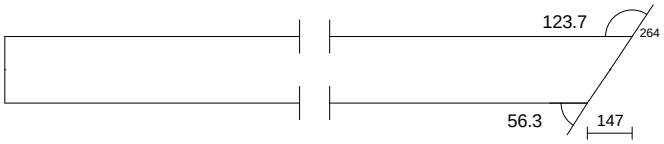


1:15

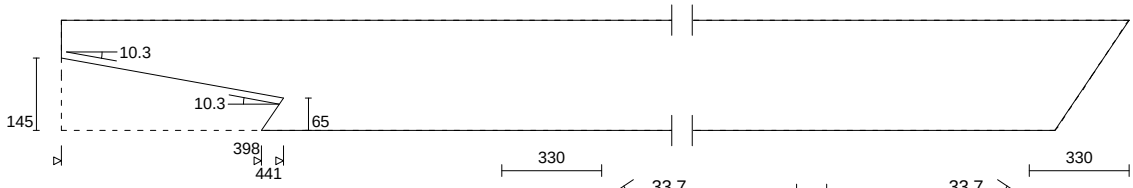


UNDERRAM

1 - 5	Dimension:	45 x 220
	Kvalitet:	C24
	Längd total:	5086 mm
	Längd centrum:	4756 mm
	Antal per konstruktion:	1 st
	Antal totalt:	7 st

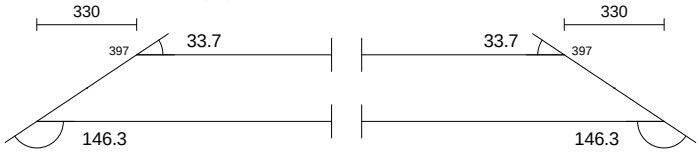


MELLANBJ.

12 - 17	Dimension:	45 x 220
	Kvalitet:	C24
	Längd total:	5086 mm
	Längd centrum:	5086 mm
	Antal per konstruktion:	- st
	Antal totalt:	6 st

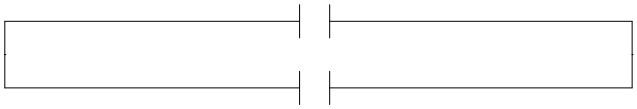

STÖDBEN

8 - 2	Dimension:	45 x 95
7 - 4	Kvalitet:	C14
	Längd total:	675 mm
	Längd centrum:	644 mm
	Antal per konstruktion:	2 st
	Antal totalt:	14 st (7v,7h)

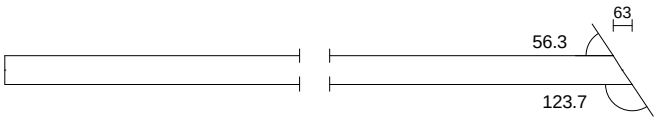

SVENSKT TRÄ


Byggbeskrivning
Enkelstugan
Snözon 2,0
Takstol Typ T1 - 2,0

RITAD KONSTR.AV	GRANSK	ARBETSNR.
JW		CO11126


KAPLISTA Sid 1(1) SKALA 1:25

Skellefteå, 20161129	KOD TYP POS	RITNINGSNUMMER	REV.
		2011	

TID: 13.44

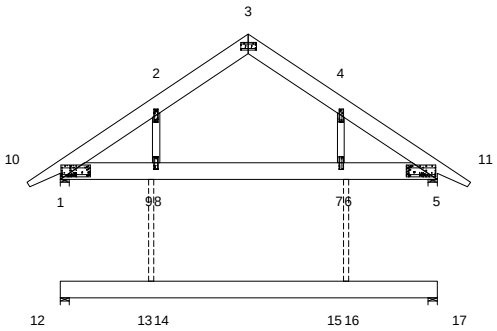


TOLERANS FÖRBANDSPLACERING: 8 mm

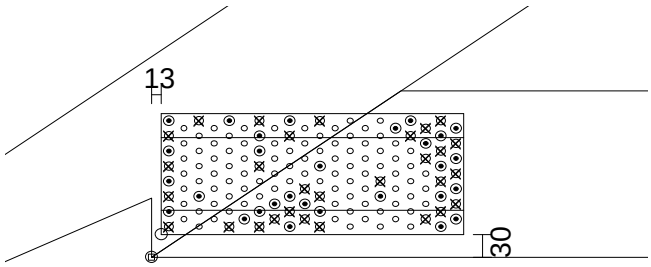


1 BMF2.0 160 x 400 100%

SPIK: 9+20 ST CNA-ankarspik 4.0x35 / SIDA SKALA 1:10

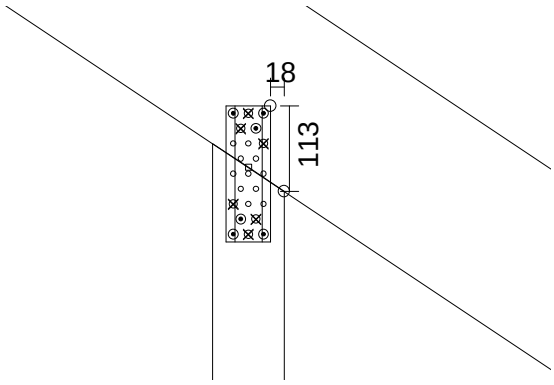


4 BMF1.5 60 x 180 67%

SPIK: 3+3 ST CNA-ankarspik 4.0x35 / SIDA SKALA 1:10

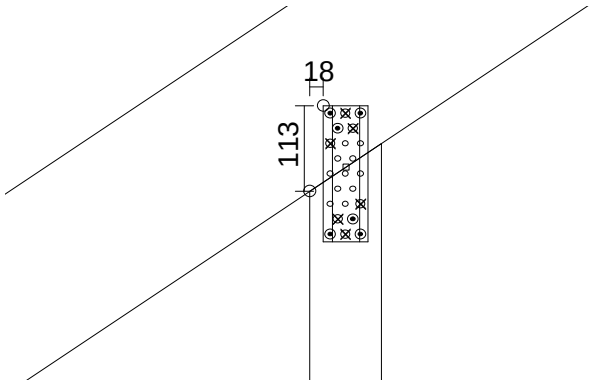


2 BMF1.5 60 x 180 67%

SPIK: 3+3 ST CNA-ankarspik 4.0x35 / SIDA SKALA 1:10

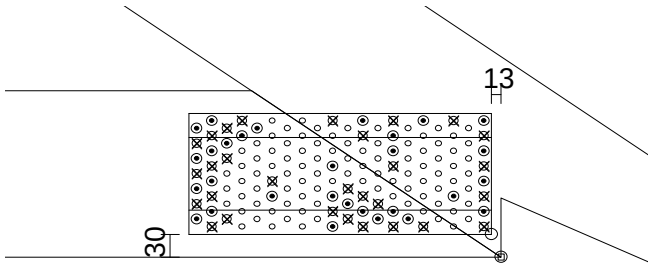


5 BMF2.0 160 x 400 100%

SPIK: 9+20 ST CNA-ankarspik 4.0x35 / SIDA SKALA 1:10

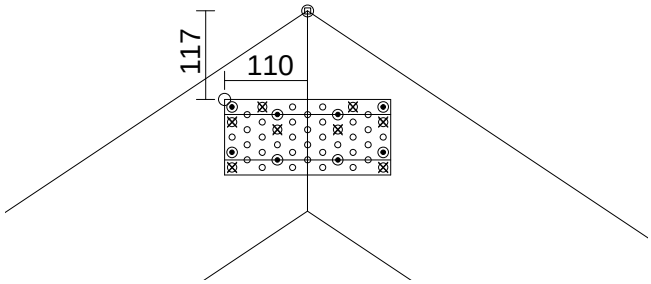

3 BMF1.5 100 x 220 97%

SPIK: 4+4 ST CNA-ankarspik 4.0x35 / SIDA SKALA 1:10

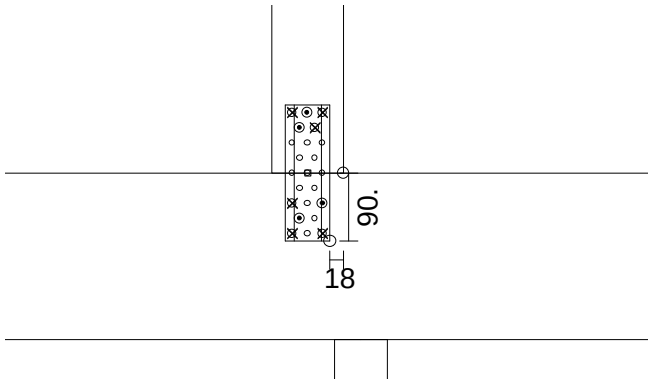

7 BMF1.5 60 x 180 80%

SPIK: 3+3 ST CNA-ankarspik 4.0x35 / SIDA SKALA 1:10

SVENSKT TRÄ

Byggbeskrivning
Enkelstugan
Snözon 2,0
Takstol Typ T1 - 2,0


SPIKFÖRBAND Sid 1(2) SKALA 1:10

RITAD KONSTR.AV	GRANSK	ARBETSNR.
JW		CO11126


Skellefteå, 20161129

KOD TYP POS	RITNINGSNUMMER	REV.
	2011	

TID: 13.44

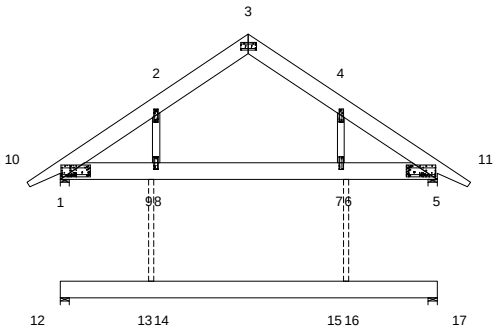

TOLERANS FÖRBANDSPLACERING: 8 mm

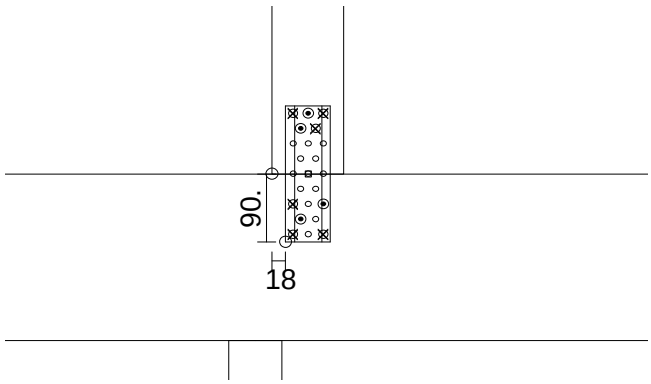

8

BMF1.5 60 x 180

SPIK: 3+3 ST CNA-ankarspik 4.0x35 / SIDA

80%

SKALA 1:10

SVENSKT TRÄ

Byggbeskrivning
Enkelstugan
Snözon 2,0
Takstol Typ T1 - 2,0

SPIKFÖRBAND

Sid 2(2)

SKALA 1:10

RITAD KONSTR.AV	GRANSK	ARBETSNR.
JW		CO11126

Skellefteå, 20161129

KOD TYP POS	RITNINGSNUMMER	REV.
	2011	

TID: 13.44

Takstolsberäkning utförd med dataprogram TrussCon

Version : 2016 SR2


Programmet utvecklat av: Construction Software Center Europe (tel 0910-87930)
Box 709
931 27 Skellefteå

BERÄKNING UTFÖRD AV

CSCE AB, Joakim Wänstedt

PROJEKT ID.

Projektkod : T1
Beställare : Byggbeskrivning
Enkelstugan
Snözon 2,0
Takstol Typ T1 - 2,0
Arbetsnr. : CO11126
Kod typ nr.:
Ritning nr.: 2011

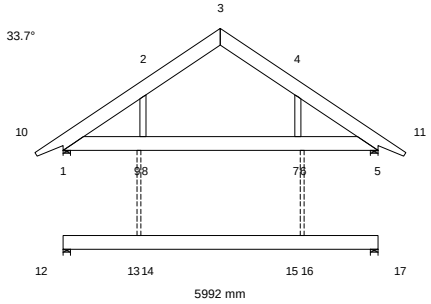

GENERELLA PROJEKTUPPGIFTER

Grundläggande dimensioneringsregler: EN 1990:2002 + A1:2005 + EKS 10
Dimensionering av träkonstruktioner: EN 1995-1-1:2004 + A1:2008 + EKS 10
Egentyngd och nyttig last : EN 1991-1-1:2002 + EKS 10
Snölast : EN 1991-1-3:2003 + EKS 10
Vindlast : EN 1991-1-4:2005 + EKS 10

Tillverkningskontroll : NEJ
Klimatklass : 2
Säkerhetsklass : 2
Lastfördelningsfaktor : 1.1
Lastbredd : 1200 mm
Antal mellanbjälkar : 1

Under rubriken "UPPGIFTER TVÄRSNITT" redovisas avvikande uppgifter
som gäller för del av konstruktion.

Konstruktionens utseende framgår av bifogad ritning.

Snittkrafter beräknas enligt 1:a ordningens deformationsteori.
Inverkan av skjuvdeformationer har medräknats.
Deformationer pga tryck vinkelrätt fiber bedöms inte
påverka systemets stabilitet och bärförmåga.
Statiska modellen är uppbyggd enligt kapitel 5.4.2 (förbandsmodell).

STANDARDLASTER

EGENTYNGD

Överram vä 1 = 650 N/m²
Överram hö 1 = 650 N/m²
Underram 1 = 300 N/m²
Stben vä 1 = 150 N/m²
Stben hö 1 = 150 N/m²

SNÖLAST

Grundvärde = 2000 N/m²
Höjd över havet = 400 m
Snörasskydd Nej
Snölinjelast vänster Ja
höger Ja

VINDLAST

Grundvärde = 730 N/m²
Byggnadsmått (mm): L=12000,B=5992,H=7000

NYTTIG LAST		Huvudomr. Från	Till	Utbred. mm	Alt.omr Från	Till	Utbred. mm
NL 2	= 1000 N/m²	7	8	2495	7	8	2495

SPECIALLASTER

EXTRA UTBREDD LAST / JUSTERADE STANDARDLASTER

Metod: 1=normal extralast, 2=ersätt denna dellast, 3=ersätt all last

Från Knut	Värde N/m²	Till Knut	Värde N/m²	Metod	Riktning	Dellast Typ
7	300	8	300	1	Vertikal	Egenlast
1	200	3	200	1	Vertikal	Egenlast
3	200	5	200	1	Vertikal	Egenlast

EXTRA PUNKTLAST

POSITIONER

Pos	Knut	Mått	Konstr.del	Rotation	Namn	Underifrån	Extra uppgifter
1	2	602	Överram vä	Ingen		NEJ	NEJ
3	3	645	Överram hö	Ingen		NEJ	NEJ
5	10	100	Överram vä	Ingen		NEJ	NEJ
6	11	-100	Överram hö	Ingen		NEJ	NEJ

VÄRDEN FÖR PUNKTLAST

Pos	Rot °	Vert N	Hori N	Moment kNm	Dellast Typ
1		1000	0	0.00	Man på överram vänster
3		1000	0	0.00	Man på överram höger
5,6		1000	0	0.00	Man på utstick

EXTRA PUNKTLAST I VARJE LASTKOMBINATION BROTTGR.

Knut	Mått	Del	LK Nr	Vert N	Hori N	Moment kNm
2	602	Överram	12	1365	0	0.00
3	645	Överram	13	1365	0	0.00
10	100	Överram	14	1365	0	0.00
11	-100	Överram	14	1365	0	0.00

LASTKOMBINATIONER

Nr	Tillstånd	Typ	Rubrik
1	Brottgräns	P	1.23*Eg.v
2	Brottgräns	M	1.09*Eg.v + 1.37*SnöMy4vä(my1hö) + 0.96*(NL1 + NL2 + NL3)
3	Brottgräns	M	1.09*Eg.v + 1.37*SnöMy4hö(my1vä) + 0.96*(NL1 + NL2 + NL3)
4	Brottgräns	M	1.09*Eg.v + 1.37*Snömy1 + 0.96*(NL1 + NL2 + NL3)
5	Brottgräns	M	1.09*Eg.v + 1.37*NL1 +0.96*(NL2 + NL3) + 0.96*Snömy1
6	Brottgräns	M	1.09*Eg.v + 1.37*NL2 +0.96*(NL1 + NL3) + 0.96*Snömy1
7	Brottgräns	M	1.09*Eg.v + 1.37*NL2 +0.96*(NL1 + NL3) + 0.96*SnöHö(0,2vä)
8	Brottgräns	M	1.09*Eg.v + 1.37*NL2 +0.96*(NL1 + NL3) + 0.96*SnöVä(0,2hö)
9	Brottgräns	K	1.09*Eg.v+1.37*Snömy1+0.96*(NL1+NL2+NL3)+.41*VindVä(0sugHö)
10	Brottgräns	K	1.09*Eg.v+1.37*Snömy1+0.96*(NL1+NL2+NL3)+.41*VindHö(0sugVä)
11	Brottgräns	K	Eg.v + 1.37*VindGavel
12	Brottgräns	Ö	1.09*Eg.v + 1.37*Man på överram vänster
13	Brottgräns	Ö	1.09*Eg.v + 1.37*Man på överram höger
14	Brottgräns	Ö	1.09*Eg.v + 1.37*Man på utstick
15	Brottgräns	M	1.09*Eg.v + 1.37*NL2 altp +0.96*(NL1 + NL3)
16	Brottgräns	K	1.09*Eg.v+1.37*SnöVä(0,2hö)+0.96*(NL1+NL2+NL3)+0.41*VindVä
17	Brottgräns	K	1.09*Eg.v+1.37*SnöHö(0,2vä)+0.96*(NL1+NL2+NL3)+0.41*VindHö
18	Brottgräns	K	1.09*Eg.v+1.37*VindVä+0.96*(NL1+NL2+NL3)+0.96*SnöVä(0,2hö)
19	Brottgräns	K	1.09*Eg.v+1.37*VindHö+0.96*(NL1+NL2+NL3)+0.96*SnöHö(0,2vä)
20	Brottgräns	M	1.09*Eg.v + 1.37*SnöMy4vä(my1hö)+0.96*(NL1+NL2altp+NL3)
21	Brottgräns	M	1.09*Eg.v + 1.37*SnöMy4hö(my1vä)+0.96*(NL1+NL2altp+NL3)
22	Bruksgräns		Eg.v + Snömy1 + 0.7*(NL1 + NL2 + NL3), 6.14inst
23	Bruksgräns		Eg.v + NL2 altp +0.7*(NL1 + NL3) + 0.7*Snömy1, 6.14inst
24	Bruksgräns		Eg.v + SnöMy4hö(my1vä) + 0.7*(NL1 + NL2 + NL3), 6.14inst
25	Bruksgräns		Eg.v + SnöMy4vä(my1hö) + 0.7*(NL1 + NL2 + NL3), 6.14inst
26	Bruksgräns		Eg.v + NL2 altp +0.7*(NL1 + NL3) + 0.7*SnöMy4hö(my1vä), 6.14inst
27	Bruksgräns		Eg.v + NL2 altp +0.7*(NL1 + NL3) + 0.7*SnöMy4vä(my1hö), 6.14inst
28	Bruksgräns		Eg.v + NL2 +0.7*(NL1 + NL3) + 0.7*SnöMy4hö(my1vä), 6.14inst
29	Bruksgräns		Eg.v + NL2 +0.7*(NL1 + NL3) + 0.7*SnöMy4vä(my1hö), 6.14inst
30	Bruksgräns		Eg.v + VindVä + 0.7*(NL1 + NL2 + NL3) + 0.7*SnöMy4vä(my1hö), 6.14inst
31	Bruksgräns		Eg.v + VindHö + 0.7*(NL1 + NL2 + NL3) + 0.7*SnöMy4hö(my1vä), 6.14inst

UPPGIFTER TVÄRSNITT

kNR: dimensionerande kontroll (1= komb. moment och normalkraft, 2= skjuvkontroll)
LK: lastkombination, KL: klimatklass, SK: säkerhetsklass

Konstruktionsdel	Dimens Från-Till	LK	kNR	kMod	gM	Tvärsnitt mm	Kval	Avstyvn mm	Max Utn	Avvik KL	Avvik SK
Överram vä 1	10- 3	2	1	0.80	1.30	45x 220	C24	400	0.56		
Överram hö 1	11- 3	3	1	0.80	1.30	45x 220	C24	400	0.56		
Underram 1	1- 5	6	1	0.80	1.30	45x 220	C24	Helt	0.39		
Stben vä 1	2- 8	7	1	0.80	1.30	45x 95	C14	Ingen	0.12		
Stben hö 1	4- 7	8	1	0.80	1.30	45x 95	C14	Ingen	0.12		
Diagonal 1	6- 16	8	1	0.80	1.30	45x 70	C14	Ingen	0.07		
Diagonal 1	9- 13	7	1	0.80	1.30	45x 70	C14	Ingen	0.07		
Mellanbj. 1	12- 17	6	1	0.80	1.30	45x 220	C24	Helt	0.33		

Urtag i virket har utförts.
Reducerat tvärsnitt nyttjas vid tvärsnittsdimensionering.
Beräkning av eventuella spänningskoncentrationer utförs och redovisas manuellt.
Spänningskoncentrationer för urtag vid upplag är medtagna i beräkningen.

FÖRBAND

Förb.typ	Fabrikat	Typgodkännandebevis
BMF2.0	Simpson Strong-Tie	Typgodk
BMF1.5	Simpson Strong-Tie	Typgodk

Knut Nr	Förb. Typ	Storlek Bredd	Längd	Max Utn	Spik Ant	Typ
1	BMF2.0	160	400	1.00	58	CNA-ankarspik 4.0x35
2	BMF1.5	60	180	0.67	12	CNA-ankarspik 4.0x35
3	BMF1.5	100	220	0.97	16	CNA-ankarspik 4.0x35
4	BMF1.5	60	180	0.67	12	CNA-ankarspik 4.0x35
5	BMF2.0	160	400	1.00	58	CNA-ankarspik 4.0x35
7	BMF1.5	60	180	0.80	12	CNA-ankarspik 4.0x35
8	BMF1.5	60	180	0.80	12	CNA-ankarspik 4.0x35

Max tillåten tolerans för förbandsplacering: 8 mm

MAX/MIN UPPLAGSREAKTIONER (N) I BRUKSGRÄNSTILLSTÅND

Knut Nr	Riktn		(LK)
1	Hori	Max: 1305	(30)
		Min: 0	(22)
1	Vert	Max: 10729	(25)
		Min: 9035	(31)
5	Vert	Max: 10729	(24)
		Min: 9032	(30)
12	Hori	Max: 0	(22)
		Min: 0	(22)
12	Vert	Max: 827	(30)
		Min: 514	(31)
17	Vert	Max: 825	(31)
		Min: 516	(30)

GRÄNSVÄRDEN DEFORMATIONSKONTROLL

Kontroll	Global	Lokal
Ramverk - överram (L/x): 6.14inst	300	300
Ramverk - underram (L/x): 6.14inst	300	300
Utstick (L/x): 6.14inst	150	150
Bjälklag (L/x): 6.14inst	300	300
Horisontell (mm):	20	-
Svikt (Sx)	2	-

KONSTRUKTIONENS STÖRSTA DEFORMATIONER

Kontroll	Lk	Längd (mm)	Tillåten L/X	Tillåten (mm)	Aktuell L/X	Aktuell (mm)
Största ögonblickliga nedböjning (6.14inst)	28	4966	300	16.6	635	7.8
Största horisontella deformation	24		-	20.0	-	0.3

MAX DEFORMATIONER (mm) I BRUKSGRÄNSTILLSTÅND

Knut/ Del	Totalt Vert	Hori	(LK)
14- 15	7.8	0.0	(26)
7- 8	7.6	0.1	(26)
2	5.1	2.7	(25)
4	5.1	-2.5	(24)
6- 7	5.3	0.2	(24)
15- 16	5.3	0.0	(24)
13- 14	5.3	0.0	(25)
8- 9	5.3	0.1	(25)
6- 16	5.1	0.1	(24)

MAX VERTIKALA DEFORMATIONER (mm) I BRUKSGRÄNSTILLSTÅND

Knut/ Del	Totalt Vert	Hori	(LK)
14- 15	7.8	0.0	(26)
7- 8	7.6	0.1	(26)
15- 16	5.3	0.0	(24)
13- 14	5.3	0.0	(25)
6- 7	5.3	0.2	(24)
8- 9	5.3	0.1	(25)

MAX HORISONTELLA DEFORMATIONER (mm) I BRUKSGRÄNSTILLSTÅND

Knut/ Del	Totalt Vert	Hori	(LK)
2	4.9	2.8	(30)
4	4.9	-2.6	(31)
11	-1.1	1.5	(24)
10	-1.4	-1.3	(30)
6	5.1	0.6	(24)
13	5.0	0.4	(27)

SVIKT PÅ GOLVBJÄLKLAG

Samverkande golvskiva: Ja
Samverkande stödbensvägg: Ja
Väggar i övervåning kläds med skivor.
Mellanbjälkar hängs upp i stödbensvägg.
Detta kan tex utföras med längsgående avväxling 45x220 som spikas med 4 st 100-34 till varje stödben. Mellanbjälkar hängs upp i avväxlingsbalkar med förankringsjärn eller bandstål.
Kontinuerlig golvbjälke: Nej

Bjälklagsplatta:
Bredd [mm] 4800

Golvbjälke:
Max spännvidd [mm] 2495

Golvspånskiva:
Tjocklek [mm] 22
E-modul böj balk [MPa] 3000
E-modul böj bredd [MPa] 3000
E-modul tryck [MPa] 2200

Glespanel:
Tjocklek [mm] 22
Bredd [mm] 95
C/C [mm] 400
E-modul böj [MPa] 8000

Styvhetsklass	Max nedböjning	Impulshastighetsrespons
S1 (låg)	2.20 mm	63.231 m/s / Ns*E-3
S2 (normal)	1.50 mm	53.553 m/s / Ns*E-3
S3 (hög)	0.80 mm	44.890 m/s / Ns*E-3
Aktuellt bjälklag:	0.43 mm	15.672 m/s / Ns*E-3

Aktuell egenfrekvens : 36 Hz

Aktuellt bjälklag uppfyller kraven för styvhetsklass: S3

UPPLAGSDATA

(1=fast, 0=fri)

Upplag nr	Knut nr	X	Z	ROT	Material
1	1	1	1	0	Trä
2	5	0	1	0	Trä
3	12	1	1	0	Trä
4	17	0	1	0	Trä

MAX/MIN UPPLAGSREAKTIONER (N) I BROTTGR. Erf. upplagsbredd anges i mm

Knut Nr	Riktn		LT P	(Nr)	LT L	(Nr)	LT M	(Nr)	LT K	(Nr)	LT Ö	(Nr)
1	Hori	Max:	0	(1)	0	(0)	0	(2)	1781	(18)	0	(12)
		Min:	0	(1)	0	(0)	0	(2)	0	(11)	0	(12)
1	Vert	Max:	5594	(1)	0	(0)	13284	(2)	13031	(10)	6387	(14)
		Min:	5594	(1)	0	(0)	6883	(15)	2287	(11)	5487	(13)
5	Vert	Max:	5594	(1)	0	(0)	13284	(3)	13031	(9)	6387	(14)
		Min:	5594	(1)	0	(0)	6883	(15)	2287	(11)	5487	(12)
12	Hori	Max:	0	(1)	0	(0)	0	(2)	0	(9)	0	(12)
		Min:	0	(1)	0	(0)	0	(2)	0	(9)	0	(12)
12	Vert	Max:	552	(1)	0	(0)	1047	(2)	1088	(18)	617	(12)
		Min:	552	(1)	0	(0)	623	(15)	194	(11)	441	(14)
17	Vert	Max:	552	(1)	0	(0)	1047	(3)	1085	(19)	617	(13)
		Min:	552	(1)	0	(0)	623	(15)	194	(11)	441	(14)

Knut Nr	Verklig mm	CSI med plåt	Erf. takstol mm	LK	Area	kc90	Erf. upplag mm	LK
1	120	-	24	2	3240	1.50	0	
5	120	-	24	2	3240	1.50	0	
12	120	-	2	2	270	1.50	0	
17	120	-	2	2	270	1.50	0	

VERTIKALA UPPLAGSREAKTIONER I ALLA DELLASTER (KARAKTERISTISKA VÄRDEN) (N)

Dellast	Knut 1	Knut 5	Knut 12	Knut 17
Egenlast	4554	4554	449	449
Snö my1vä, 0,5my1hö	5109	4840	340	305
Snö 0,5my1vä, my1hö	4840	5109	305	340
Snö my1vä,my1hö	4738	4738	307	307
Vind från vänster (0 sug hö)	599	621	132	-24
Vind från höger (0 sug vä)	622	600	-25	131
Vind mot gavel	-1649	-1649	-199	-199
Nyttig last 1	0	0	0	0
Nyttig last 2	1400	1400	97	97
Nyttig last 3	0	0	0	0
Nyttig last 2 alt plac	1400	1400	97	97
Snö my1vä, 0,2my1hö	3921	1764	324	45
Snö 0,2my1vä, my1hö	1764	3921	45	324
Vind från vänster	255	17	143	-121
Vind från höger	19	258	-123	140
Man på överram vänster	0	0	0	0
Man på utstick	0	0	0	0
Man på överram höger	0	0	0	0