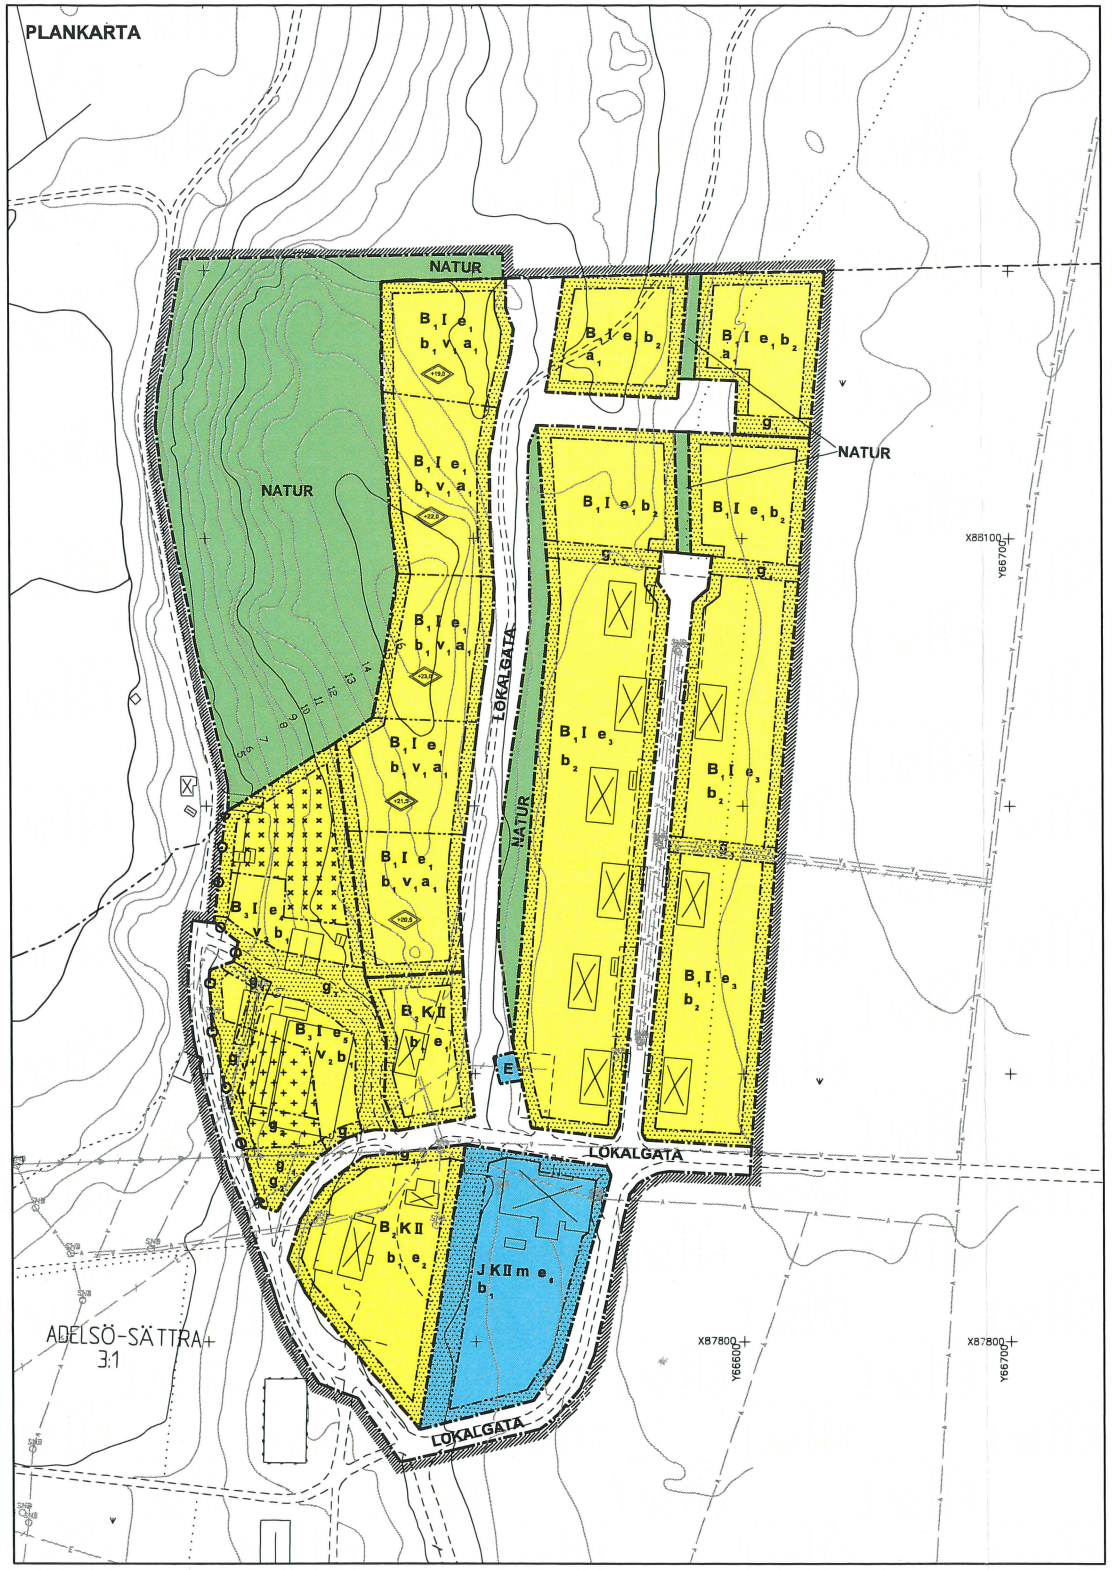


Grundkarta över Adelsö-Sättra 3:1 m.fl i Ekerökommun,

Upprättad 2009-06-29 av Arctan AB i Östersund

Uppdragsnr: 09009

Marcus Amrén

Plansystem: ST 74.0 gon 65--1
Höjdsystem: RH00
Ekvidistans 1m
Kvalitetsklass: HMK Klass V
Skala 1:1000 (A0)

Ej och VA-ledningar är ej fullständigt redovisad


Skala 1:1000 (A1)

10 0 10 20 30 40 50 100 m

Teckenförklaring

- Fastighetsgräns
- Strandskyddsgräns
- Vägkant
- Stig/Elljusspår
- Stig/Elljusspår
- Stig/Elljusspår
- Ägoslagsgräns
- Strandkant
- Nivåkurver
- Spillvattenledning
- Spill tryckledning
- Vattenledning
- Dagvattenledning
- El markledningsläsäkert läge)
- Trakt.namn
- ADELSÖ-SÄTTRA 3:1 Fastighetsbeteckning
- Hus takliv
- Uthus takliv
- Äng/Åker
- Spillbrunn
- Dagvattenbrunn
- Koordinatkryss

Planområdet

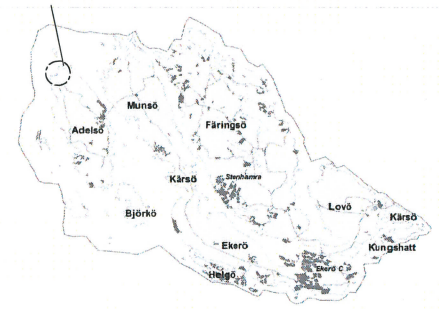

PLANBESTÄMMELSER

Följande gäller inom områden med nedanstående beteckningar. Där beteckning saknas gäller bestämmelsen inom hela planområdet. Endast angiven användning och utformning är tillåten.

GRÄNSBETECKNINGAR

- Detaljplanegränsen ligger i skrafferingen innerkant
- Användningsgräns
- Egenskapsgräns

ANVÄNDNING AV MARK

Allmän platsmark
- NATUR — Naturmark
- LOKALGATA — Lokal trafik

Kvartersmark
- B_1 — Bostäder, en- och tvåfamiljshus
- B_2 — Bostäder, enfamiljshus
- B_1K — Bostäder, kontor
- JK — Småindustri, kontor
- E — Transformatorstation

UTNYTTJANDEGRAD

- e_1 Största tillåtna byggnadsarea för huvudbyggnad är 280 kvm per tomtplats. Tomtplats får bebyggas med maximalt en huvudbyggnad med en lägenhet. Största tillåtna byggnadsarea för komplementbyggnader är 60 kvm. Minsta tomtstorlek är 2000 kvm. Maximalt två komplementbyggnader per tomtplats.
- e_2 Största tillåtna byggnadsarea är 500 kvm. Tomtplats får bebyggas med maximalt en huvudbyggnad med maximalt tre lägenheter. Minsta tomtstorlek är 3000 kvm. Maximalt tre komplementbyggnader.
- e_3 Största tillåtna byggnadsarea är 250 kvm per tomtplats. Tomtplats får bebyggas med maximalt en huvudbyggnad med maximalt två lägenheter per tomtplats. Minsta tomtstorlek är 1200 kvm. Maximalt två komplementbyggnader per tomtplats.
- e_4 Största tillåtna byggnadsarea för huvudbyggnad är 120 kvm. Området får bebyggas med maximalt två huvudbyggnader med en lägenhet/huvudbyggnad. Största tillåtna byggnadsarea för komplementbyggnader är totalt 80 kvm. Minsta tomtstorlek är 400 kvm. Maximalt tre komplementbyggnader. Området ska ges en sammanhållen utformning lika område betecknat e5
- e_5 Största tillåtna byggnadsarea för huvudbyggnad är 120 kvm. Området får bebyggas med maximalt tre huvudbyggnader med en lägenhet/huvudbyggnad. Största tillåtna byggnadsarea för komplementbyggnader är totalt 200 kvm. Minsta tomtstorlek är 400 kvm. Maximalt fyra komplementbyggnader. Området ska ges en sammanhållen utformning lika område betecknat e4
- e_6 Största tillåtna byggnadsarea är 1500 kvm.

BEGRÄNSNINGAR AV MARKENS BEBYGGANDE

- Marken får inte bebyggas
- Marken får endast bebyggas med garage och förråd
- Marken får endast bebyggas med förråd
- g_1 Marken skall vara tillgänglig för gemensamma underjordiska ledningar
- g_2 Marken ska vara tillgänglig för gemensamt garage/p-plats för kvartersmarken B3
- g_3 Marken ska vara tillgänglig för gemensamhetsanläggning för tillfart för fastigheter inom kvartersmarken B3

PLACERING, UTFORMNING, UTFÖRANDE, ANORDNANDE

- I, II Högsta tillåtet antal våningar
- v_1 Utöver angivet våningsantal får slutningsvåning anordnas om terrängen så medger, dock ej mot väster
- v_2 Utöver angivet våningsantal får slutningsvåning anordnas. Anordnas slutningsvåning får vind ej inredas
- b_1 Takvatten skall så långt möjligt infiltreras
- b_2 Dagvatten ska anslutas till befintligt dagvattennät
- +42 Högsta nockhöjd i meter över nollplanet
- Körbar in- och utfart får ej anordnas. Inom hela planområdet gäller att bebyggelsen i sin utformning ska anpassas till de karaktärsdrag och den byggnadssätt som gårdens övriga byggnader har.

STÖRNINGSSKYDD

- m Verksamheten får inte vara störande för närliggande bostäder. Ekvivalentnivån för buller vid kvartersgräns för bostäder får inte överskrida 40 dB(A)

ADMINISTRATIVA BESTÄMMELSER

Genomförandetid
Genomförandetiden är 10 år från den dag planen vinner laga kraft
Huvudmannaskap
Kommunen är inte huvudman för allmän plats
Lov med villkor
- a_1 Bygglov får ej lämnas förrän anslutande lokalgata och VA anläggning är utbyggda

EKERÖ KOMMUN

ANTAGANDE

NORMALT FÖRFARANDE

DETALJPLAN FÖR
SÄTTRA GÅRD, DEL AV FAST ADELSÖ-SÄTTRA 3:1
I EKERÖ KOMMUN, STOCKHOLMS LÄN

UPPRÄTTAD I 10 APRIL 2010 AV ULF ALEXANDERSSON AB
I SAMARBETE MED STADSARKITEKTKONTORET I EKERÖ KOMMUN
REV 15 OKT 2012

JOHAN HAGLAND — **MILJÖ- OCH STADSBYGGNADSCHEF**
JOHANNA WULFF — **PLANARKITEKT**

Beslutsdatum	Instans
Godkännande XX-XX-XX	BN
Antagande XX-XX-XX	
Laga kraft XX-XX-XX	
Plannummer XXX	
Diarienummer 2004.28.214	