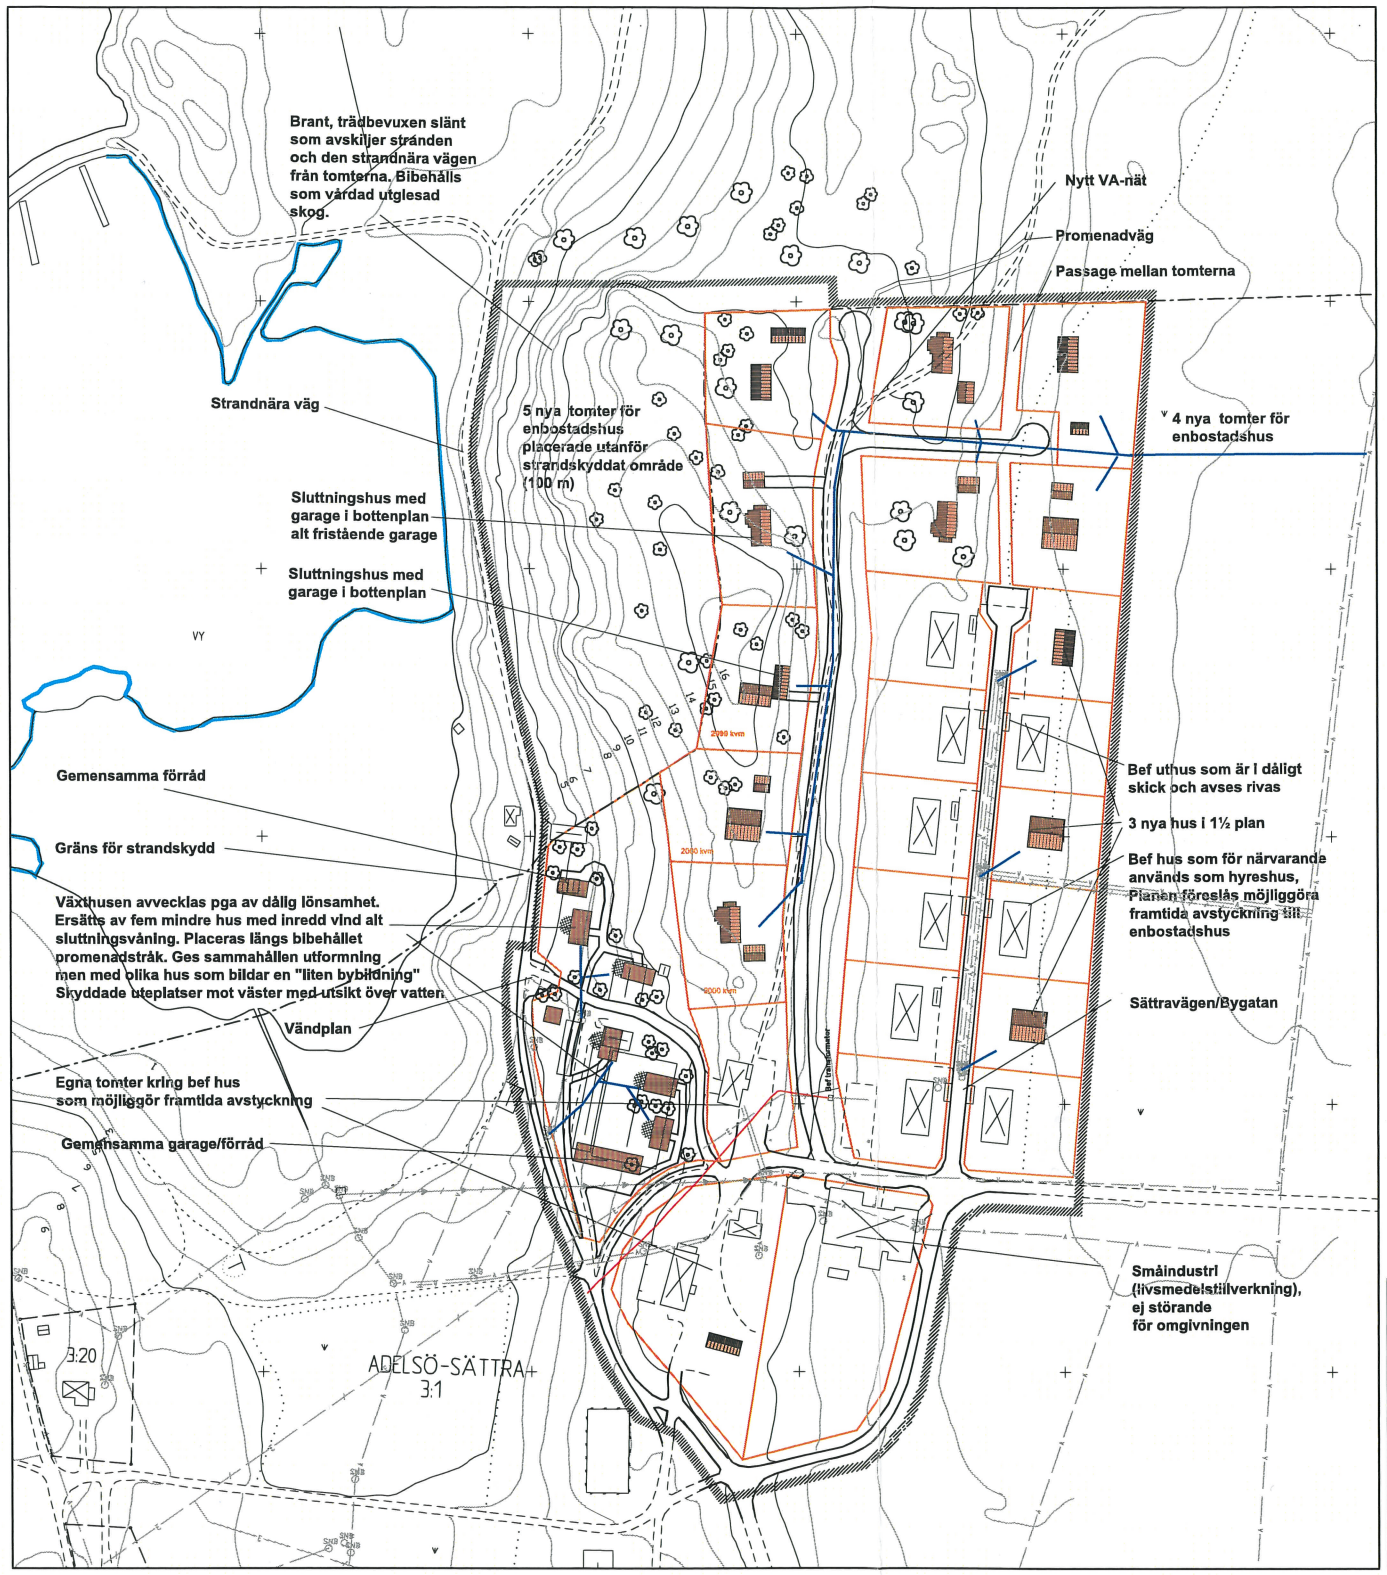


Grundkarta över Adelsö-Sättra 3:1 m.fl i Ekerökommun.

Upprättad 2009-06-29 av Arctan AB i Östersund
Uppdragsnr: 09009

Marcus Amrén

Plansystem: ST 74 8 gon 65-1
Höjdsystem: RHOO
Ekvidistan: 1m
Kvalitetsklass: HMK Klass V
Skala 1:1000 (A0)


El och VAO-ledningar är ej fullständigt redovisad

Skala 1:1000 (A1)
10 0 10 20 30 40 50 100 m

Teckenförklaring

- Fastighetsgräns
- Strandskyddsgräns
- Vägkant
- Stig/Elljusspår
- Stig/Elljusspår
- Stig/Elljusspår
- Ägoslagsgräns
- Strandkant
- Nivåkurvor
- Spillvattenledning
- Spill tryckledning
- Vattenledning
- Dagvattenledning
- El markledningsskärt läge)
- ADELSÖ-SÄTTRA 3:1 Traktnamn
- Fastighetsbeteckning
- Hus takliv
- Uthus takliv
- Ång/Åker
- Spillbrunn
- Dagvattenbrunn
- Koordinatkryss

Planområdet

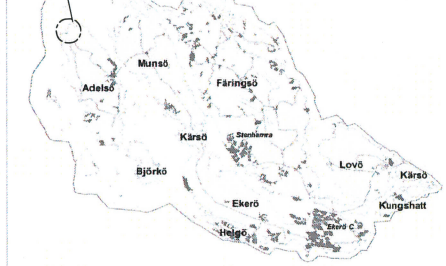

Illustration

EKERÖ KOMMUN

ANTAGANDE

NORMALT FÖRFARANDE

DETALJPLAN FÖR
SÄTTRA GÅRD, DEL AV FAST ADELSÖ-SÄTTRA 3:1
I EKERÖ KOMMUN, STOCKHOLMS LÄN

Beslutsdatum	Instans
Godkännande XX-XX-XX	BN
Antagande XX-XX-XX	
Laga kraft XX-XX-XX	

Plannummer XXX

Diarienummer 2004.28.214

UPPRÄTTAD I 10 APRIL 2010 AV ULF ALEXANDERSSON AB
I SAMARBETE MED STADSARKITEKTKONTORET I EKERÖ KOMMUN
REV 15 OKT 2012

JOHAN HAGLAND
MILJÖ- OCH STADSBYGGNADSCHEF

JOHANNA WULFF
PLANARKITEKT